


PLANTA BAIXA — LEVANTAMENTO CADASTRAL

Situação existente, redesenhada a partir do croqui de medição · cotas em metros · escala 1:50 em A3

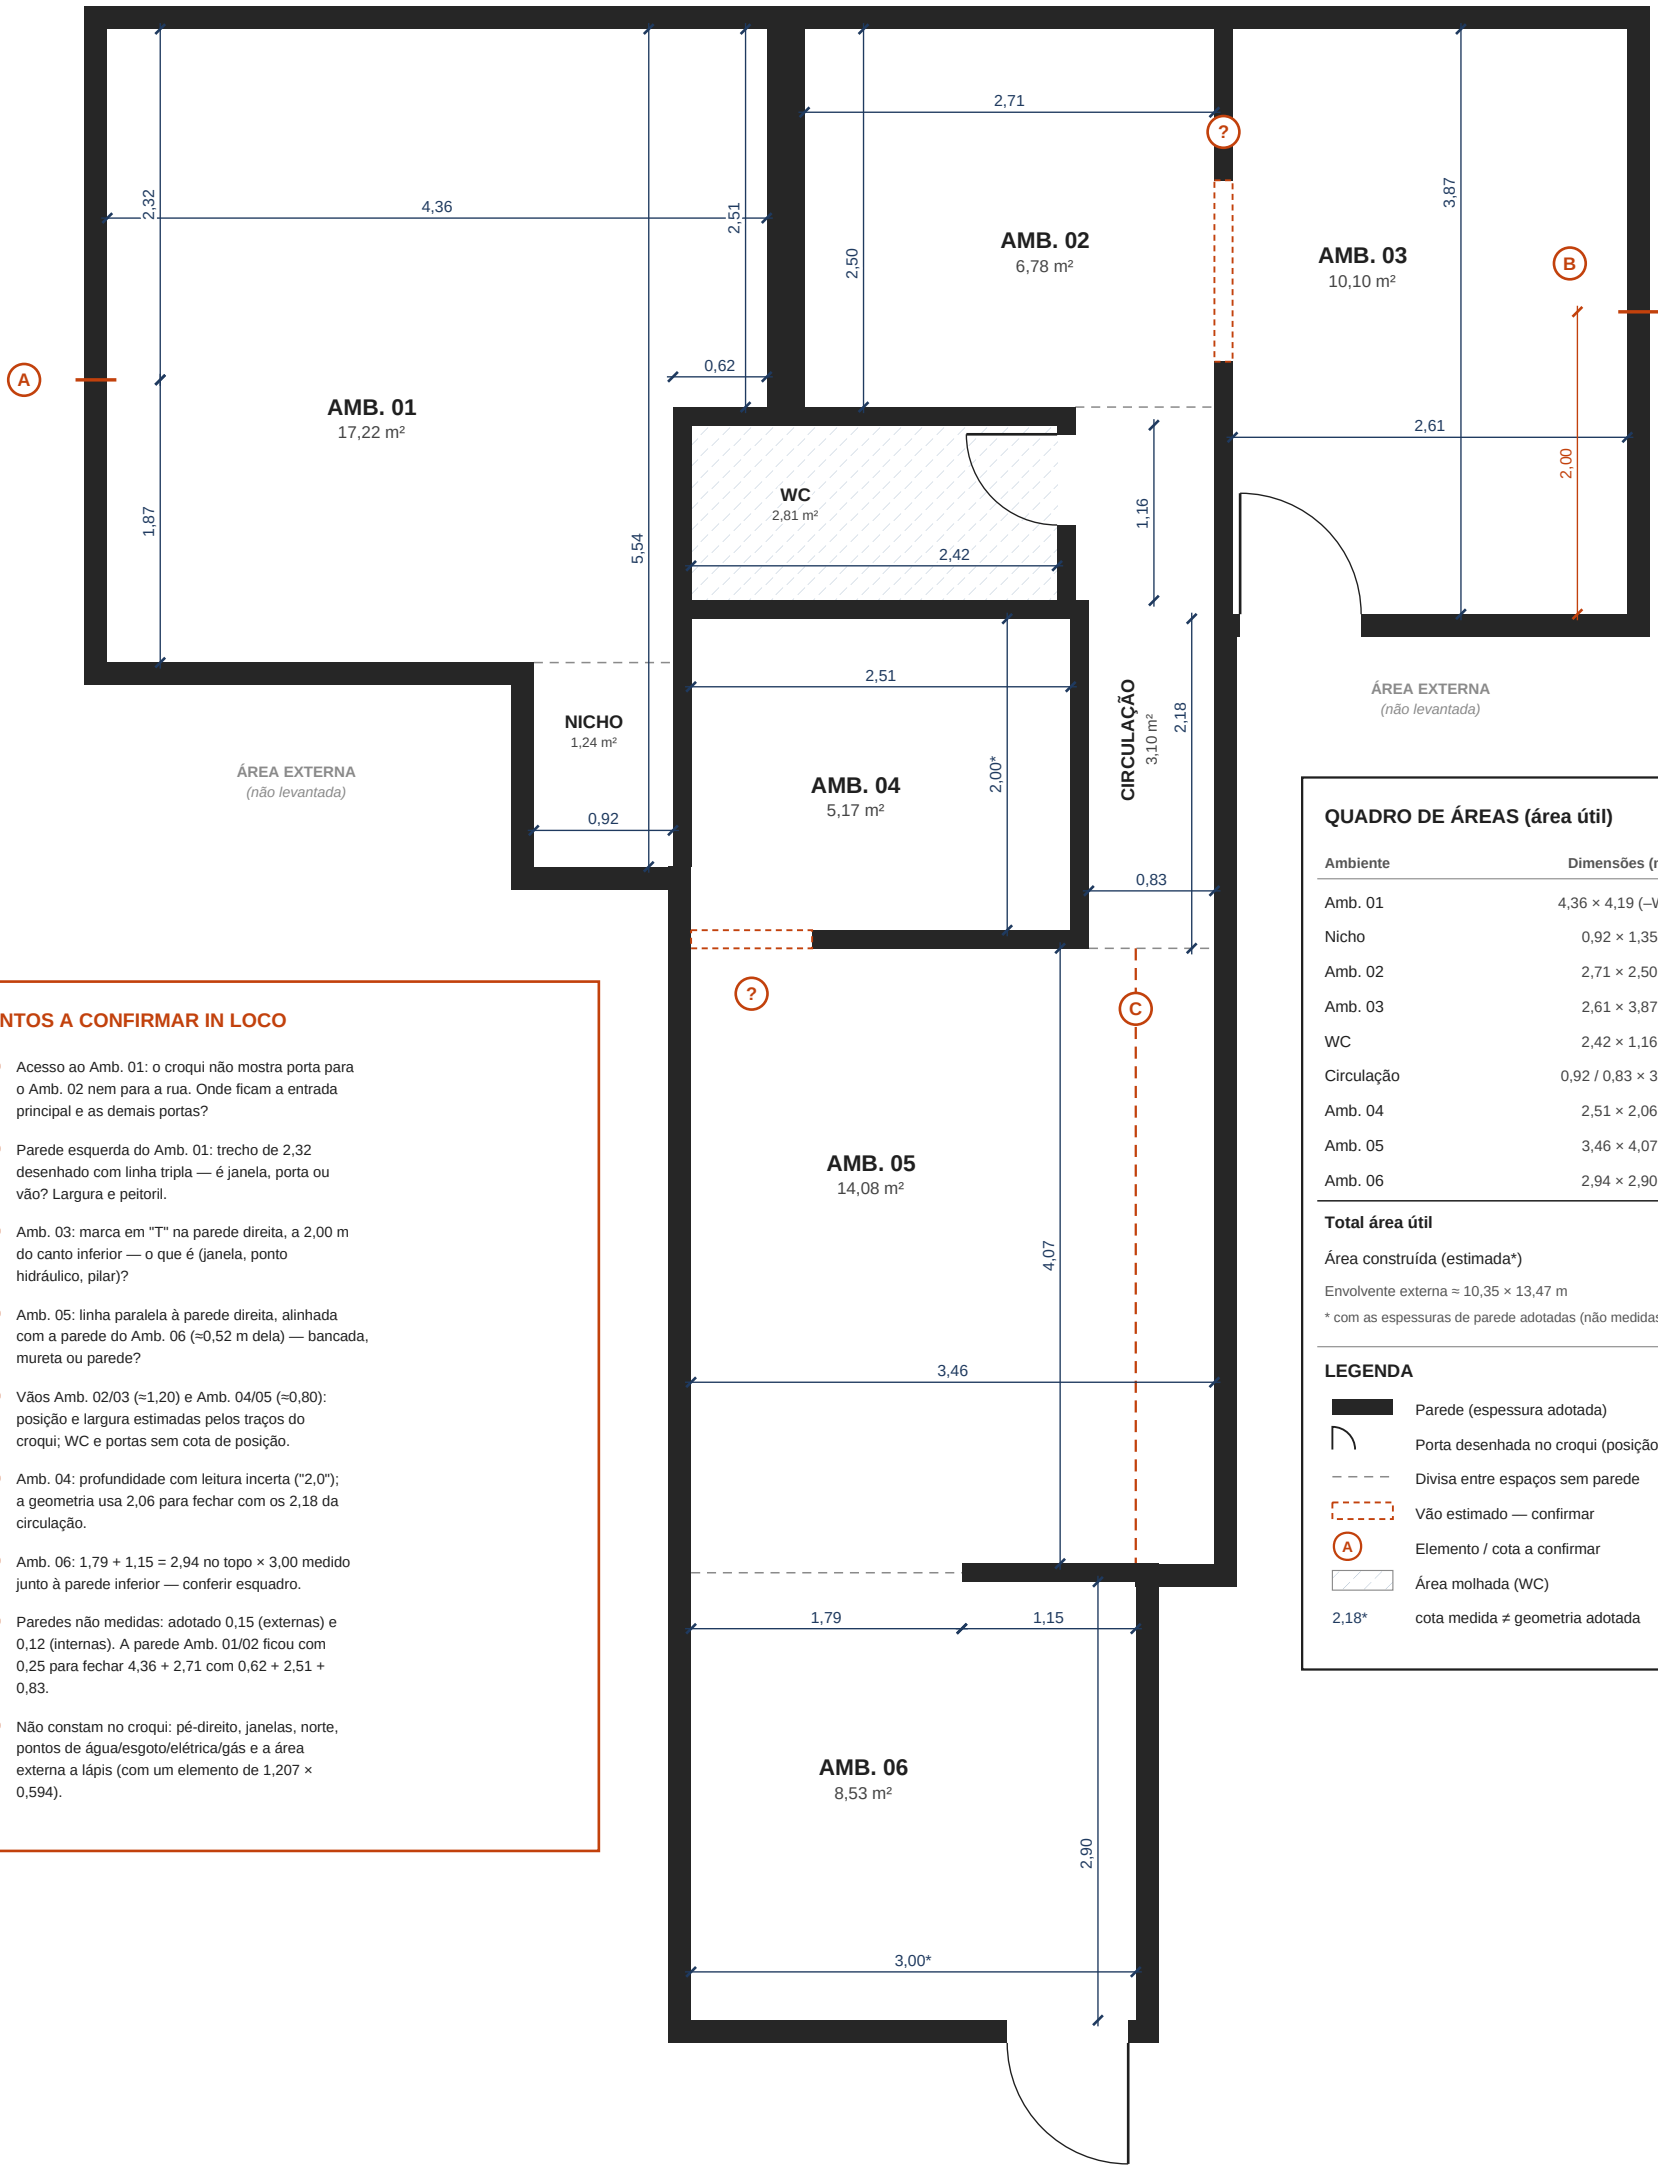

PONTOS A CONFIRMAR IN LOCO

- 1 Acesso ao Amb. 01: o croqui não mostra porta para o Amb. 02 nem para a rua. Onde ficam a entrada principal e as demais portas?
- A Parede esquerda do Amb. 01: trecho de 2,32 desenhado com linha tripla — é janela, porta ou vão? Largura e peitoril.
- B Amb. 03: marca em "T" na parede direita, a 2,00 m do canto inferior — o que é (janela, ponto hidráulico, pilar)?
- C Amb. 05: linha paralela à parede direita, alinhada com a parede do Amb. 06 (≈0,52 m dela) — bancada, mureta ou parede?
- ? Vãos Amb. 02/03 (≈1,20) e Amb. 04/05 (≈0,80): posição e largura estimadas pelos traços do croqui; WC e portas sem cota de posição.
- 2 Amb. 04: profundidade com leitura incerta ("2,0"); a geometria usa 2,06 para fechar com os 2,18 da circulação.
- 3 Amb. 06: 1,79 + 1,15 = 2,94 no topo × 3,00 medido junto à parede inferior — conferir esquadro.
- 4 Paredes não medidas: adotado 0,15 (externas) e 0,12 (internas). A parede Amb. 01/02 ficou com 0,25 para fechar 4,36 + 2,71 com 0,62 + 2,51 + 0,83.
- 5 Não constam no croqui: pé-direito, janelas, norte, pontos de água/esgoto/elétrica/gás e a área externa a lápis (com um elemento de 1,207 × 0,594).

QUADRO DE ÁREAS (área útil)

Ambiente	Dimensões (m)	Área (m²)
Amb. 01	4,36 × 4,19 (–WC)	17,22
Nicho	0,92 × 1,35	1,24
Amb. 02	2,71 × 2,50	6,78
Amb. 03	2,61 × 3,87	10,10
WC	2,42 × 1,16	2,81
Circulação	0,92 / 0,83 × 3,58	3,10
Amb. 04	2,51 × 2,06	5,17
Amb. 05	3,46 × 4,07	14,08
Amb. 06	2,94 × 2,90	8,53
Total área útil		69,03
Área construída (estimada*)		≈ 79,2
Envolvente externa ≈ 10,35 × 13,47 m		
* com as espessuras de parede adotadas (não medidas).		

LEGENDA

- Parede (espessura adotada)
- Porta desenhada no croqui (posição aprox.)
- Divisa entre espaços sem parede
- Vão estimado — confirmar
- Elemento / cota a confirmar
- Área molhada (WC)
- 2,18* cota medida ≠ geometria adotada

ESCALA 1:50



SAFRAN ALIMENTOS LTDA

Safran Congelados

CNPJ 31.511.591/0001-95

Isabel C. P. Cavalcante · Victor A. C. Costa ·
Glaucos A. C. Costa

LEVANTAMENTO CADASTRAL — PLANTA BAIXA

Imóvel da cozinha de produção (≈ 80 m²)

Rua Fernando Mendes Pinto, 05 — Barro Duro

Maceió/AL — CEP 57045-065

Redesenho do croqui de medição manual. Documento de trabalho:
conferir in loco antes de usar em projeto, licenciamento ou obra.

ESCALA

1:50

UNIDADE

metro

DATA

05/10/2026

FOLHA

A3

REVISÃO

R00

STATUS

PRELIMINAR