


ANTES x DEPOIS — FLUXOS, LAYOUT E INTERVENÇÕES (v2)


Safran Congelados · imóvel do Barro Duro · sobre a planta R02 · escala 1:75 · equipamentos com medidas típicas (conferir com as propostas) · nicho fechado; cozinha com portão para a rua principal

ANTES (hoje)

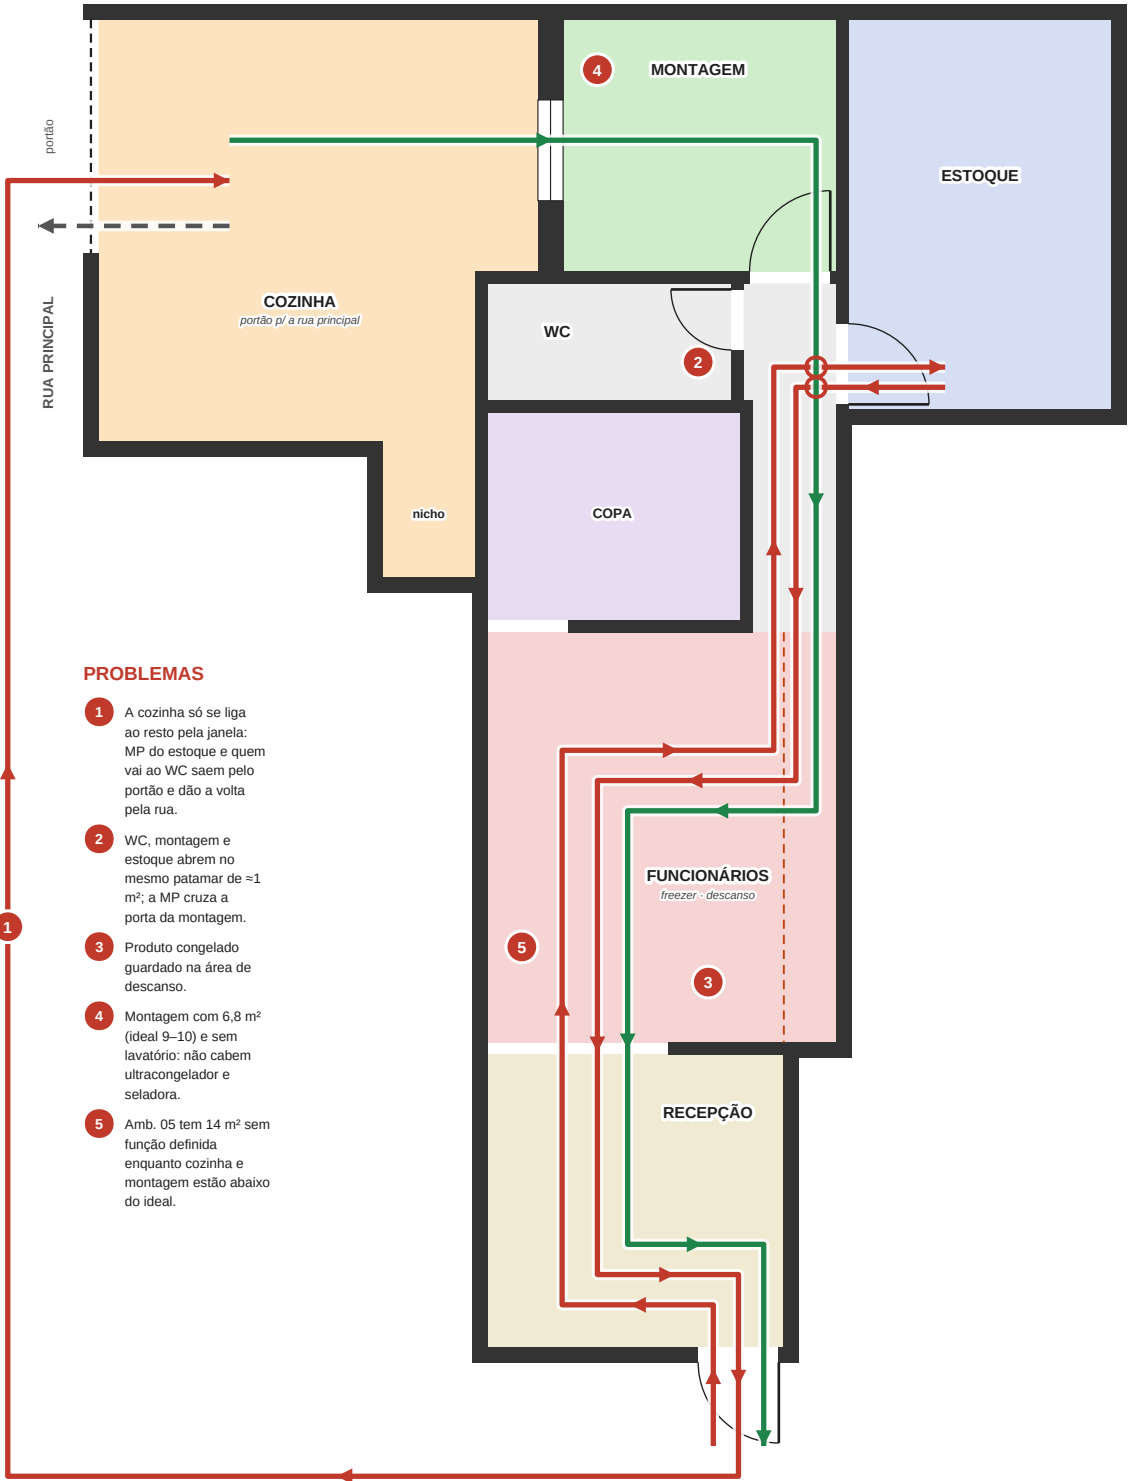

volta pela rua (esquemático)

DEPOIS (proposta)

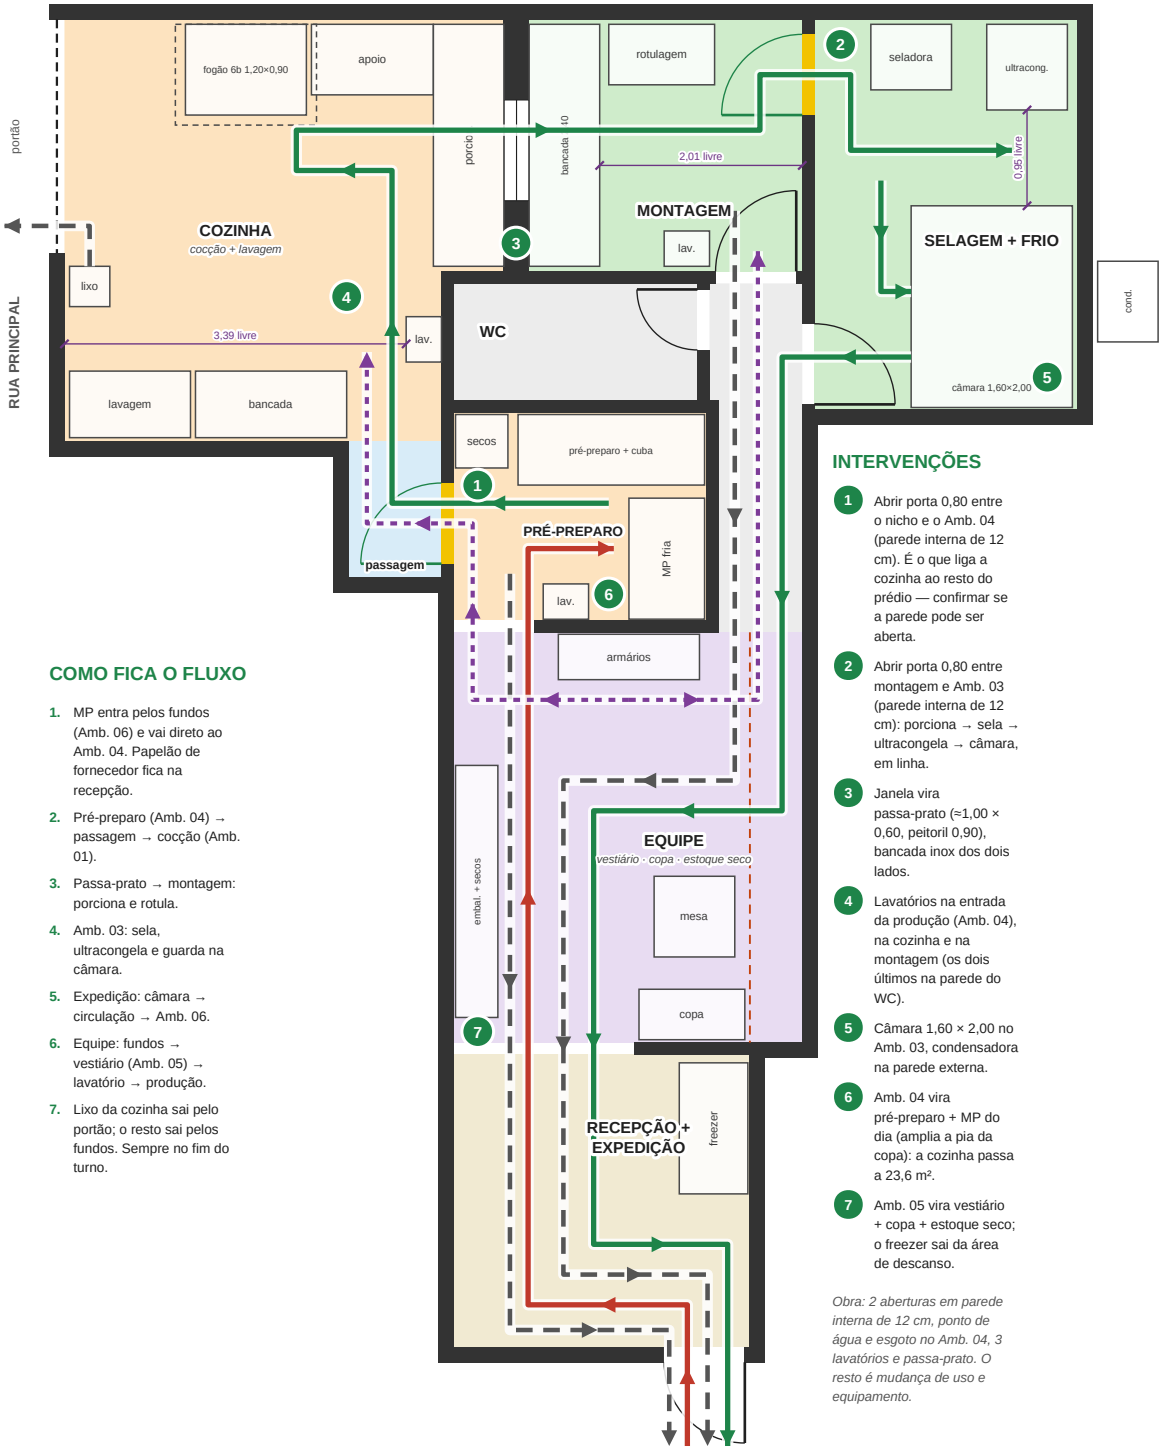

INTERVENÇÕES

- 1 Abrir porta 0,80 entre o nicho e o Amb. 04 (parede interna de 12 cm). É o que liga a cozinha ao resto do prédio — confirmar se a parede pode ser aberta.
- 2 Abrir porta 0,80 entre montagem e Amb. 03 (parede interna de 12 cm): porciona → sela → ultracongela → câmara, em linha.
- 3 Janela vira passa-prato (≈1,00 × 0,60, peitoril 0,90), bancada inox dos dois lados.
- 4 Lavatórios na entrada da produção (Amb. 04), na cozinha e na montagem (os dois últimos na parede do WC).
- 5 Câmara 1,60 × 2,00 no Amb. 03, condensadora na parede externa.
- 6 Amb. 04 vira pré-preparo + MP do dia (amplia a pia da copa): a cozinha passa a 23,6 m².
- 7 Amb. 05 vira vestiário + copa + estoque seco; o freezer sai da área de descanso.

Obra: 2 aberturas em parede interna de 12 cm, ponto de água e esgoto no Amb. 04, 3 lavatórios e passa-prato. O resto é mudança de uso e equipamento.

LEGENDA

- Cozinha (pré-preparo, cocção, lavagem)
- Montagem e frio (área limpa)
- Passagem / barreira
- Armazenagem
- Equipe (vestiário, copa, descanso)
- Recepção / expedição
- Uso misto (problema)
- WC / circulação
- Matéria-prima
- Alimento / produto
- Lixo
- Equipe
- Cruzamento sujo × limpo
- Abrir vão (porta nova em verde)
- Espaço livre entre equipamentos (m)

TRAJETOS (m)

	Antes	Depois
MP estocada → pré-preparo	38 (22 na rua)	< 1
Cozinha → WC	36 (21 na rua)	13
Porcionamento → frio	10	5
Cruzamentos sujo × limpo	2	0

Trechos na rua são esquemáticos (mínimo): a volta real depende do quarteirão.

ÁREA POR SETOR (m²)

	Ideal*	Antes	Depois
Cozinha	20–24	18,46	23,63
Montagem + selagem/UC	9–10	6,78	≈ 11
Armazenagem	11–12	10,10	≈ 9 (3 salas)
Recepção / expedição	6–8	8,53	8,53
Equipe (sem WC)	6–10	5,17	≈ 11
Uso misto	—	14,08	—

* Estimativa para ~150 refeições/dia (capacidade já demonstrada), com equipamentos ocupando ≈ 40% da área de produção e ≈ 60% da de armazenagem.

ESCALA 1:75

